



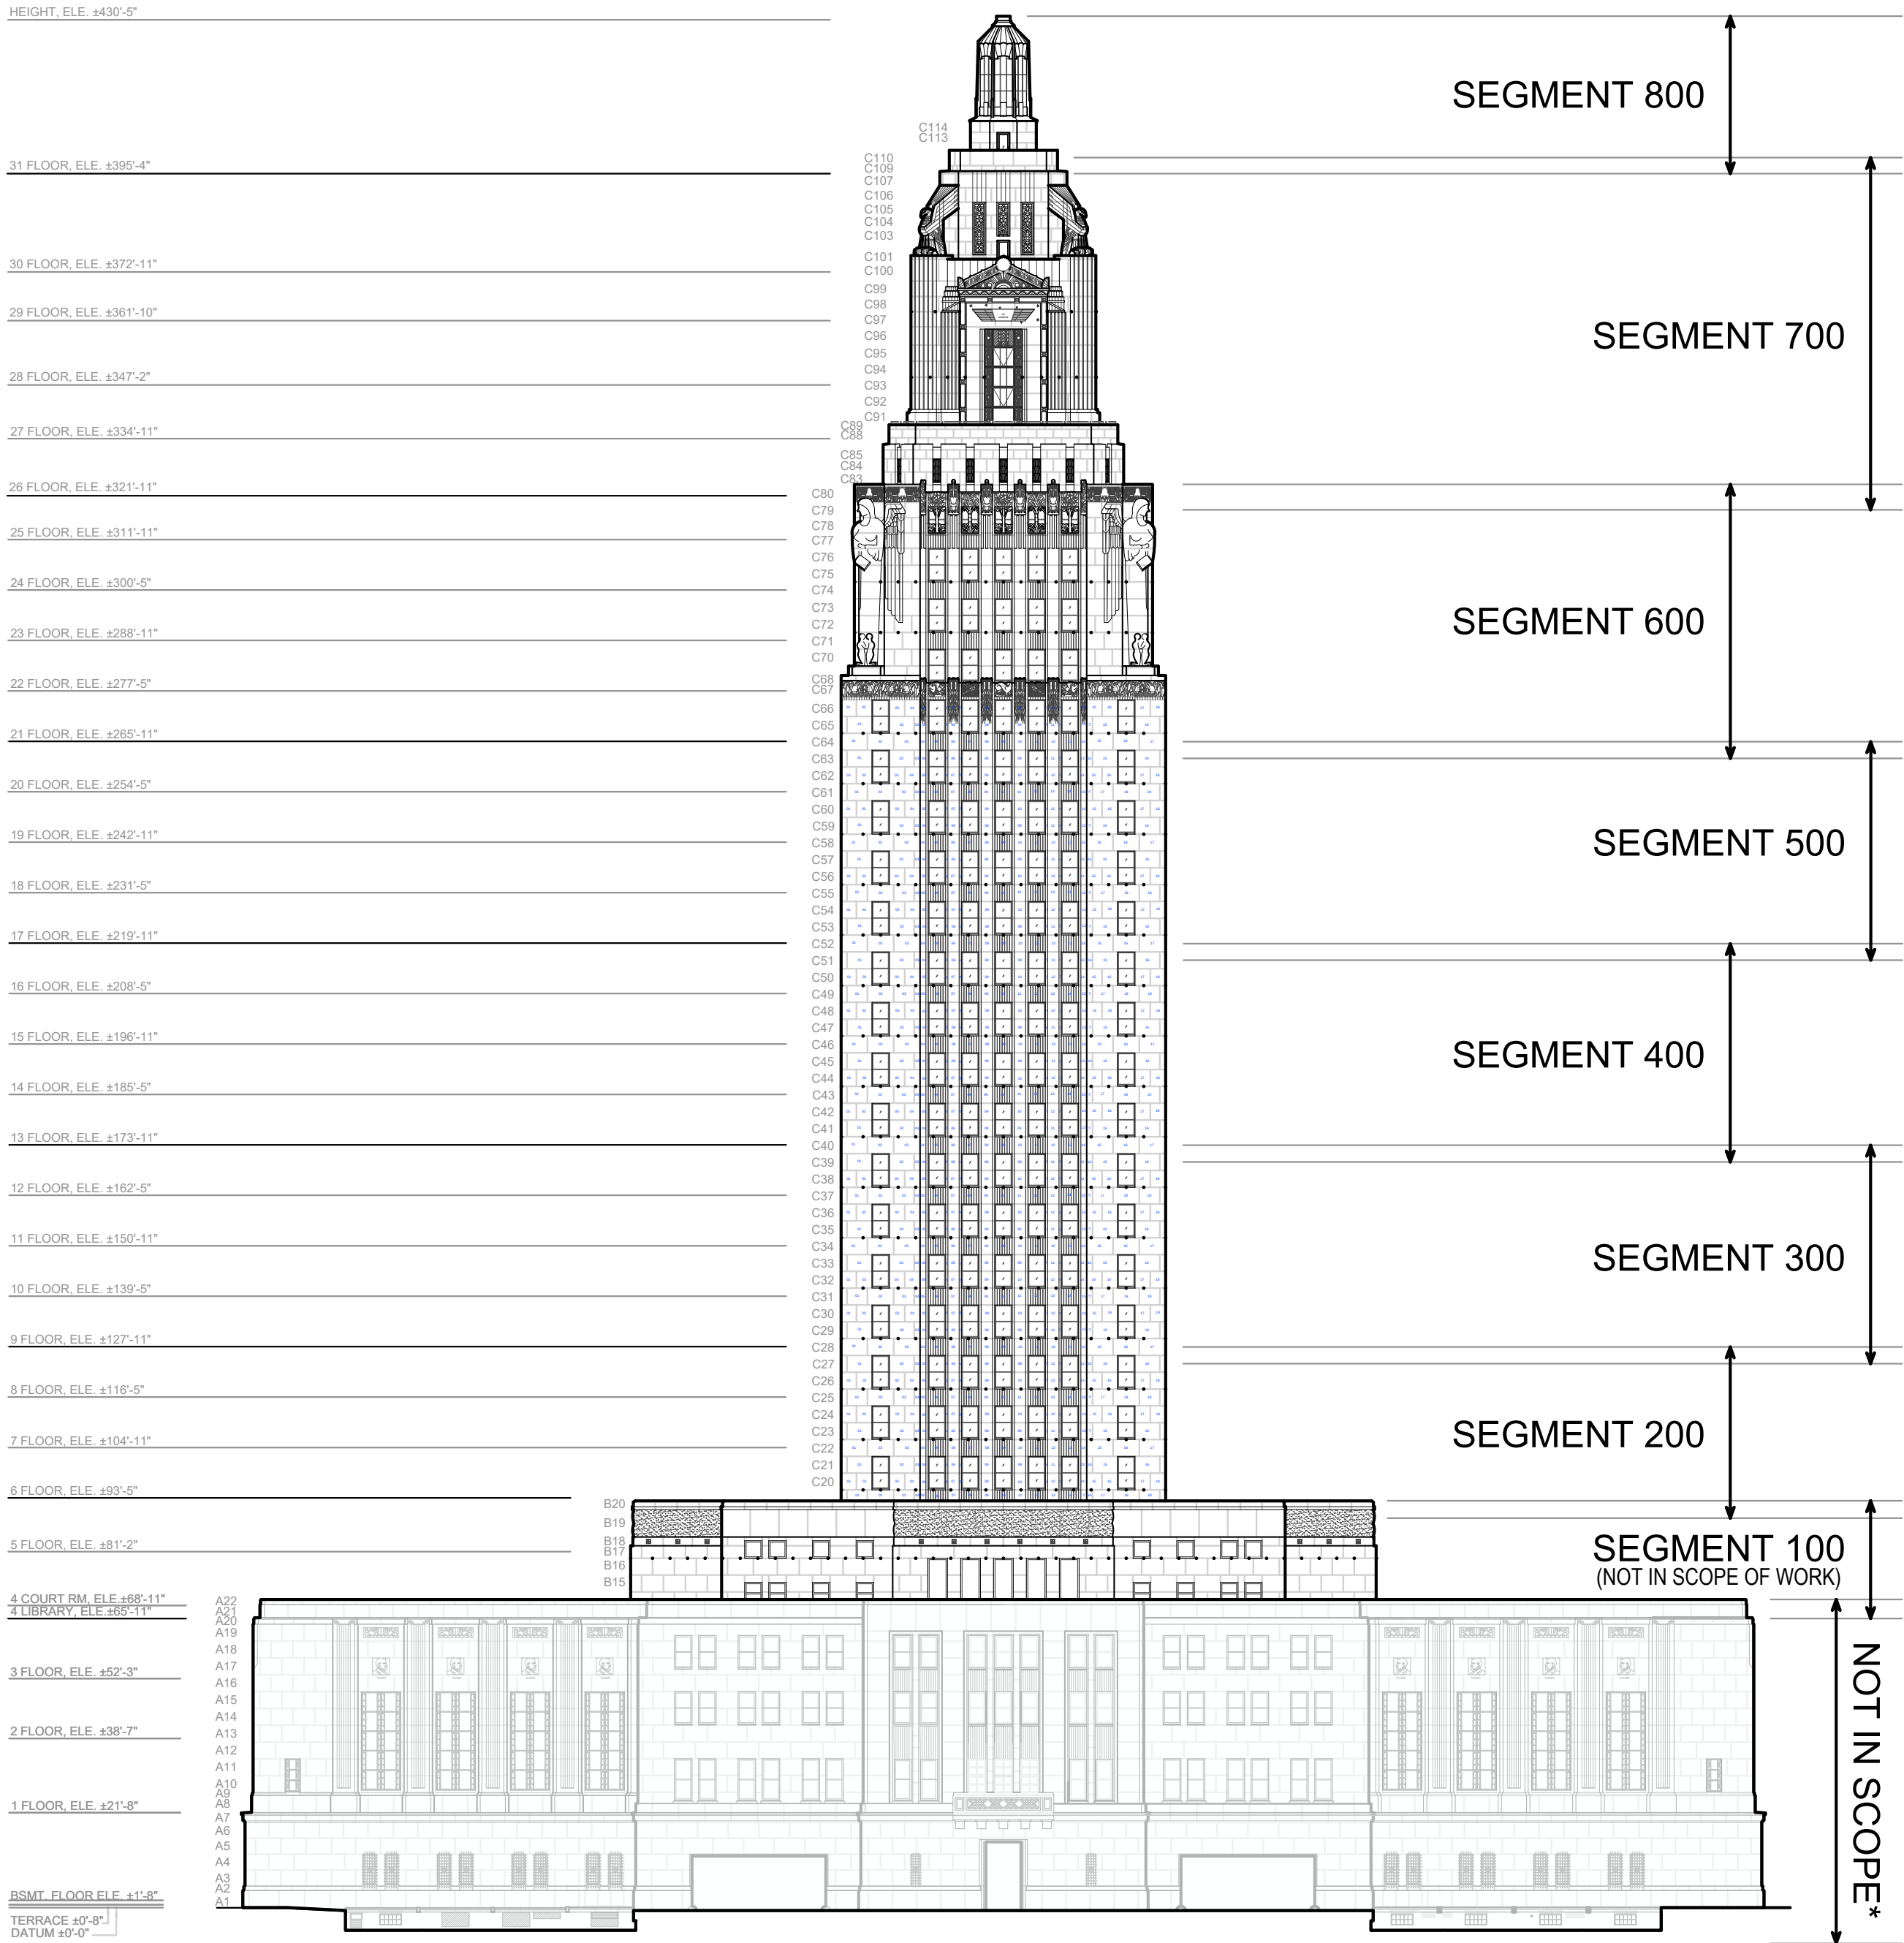


1 NORTH KEY ELEVATION
SCALE: 1/32"=1'-0"

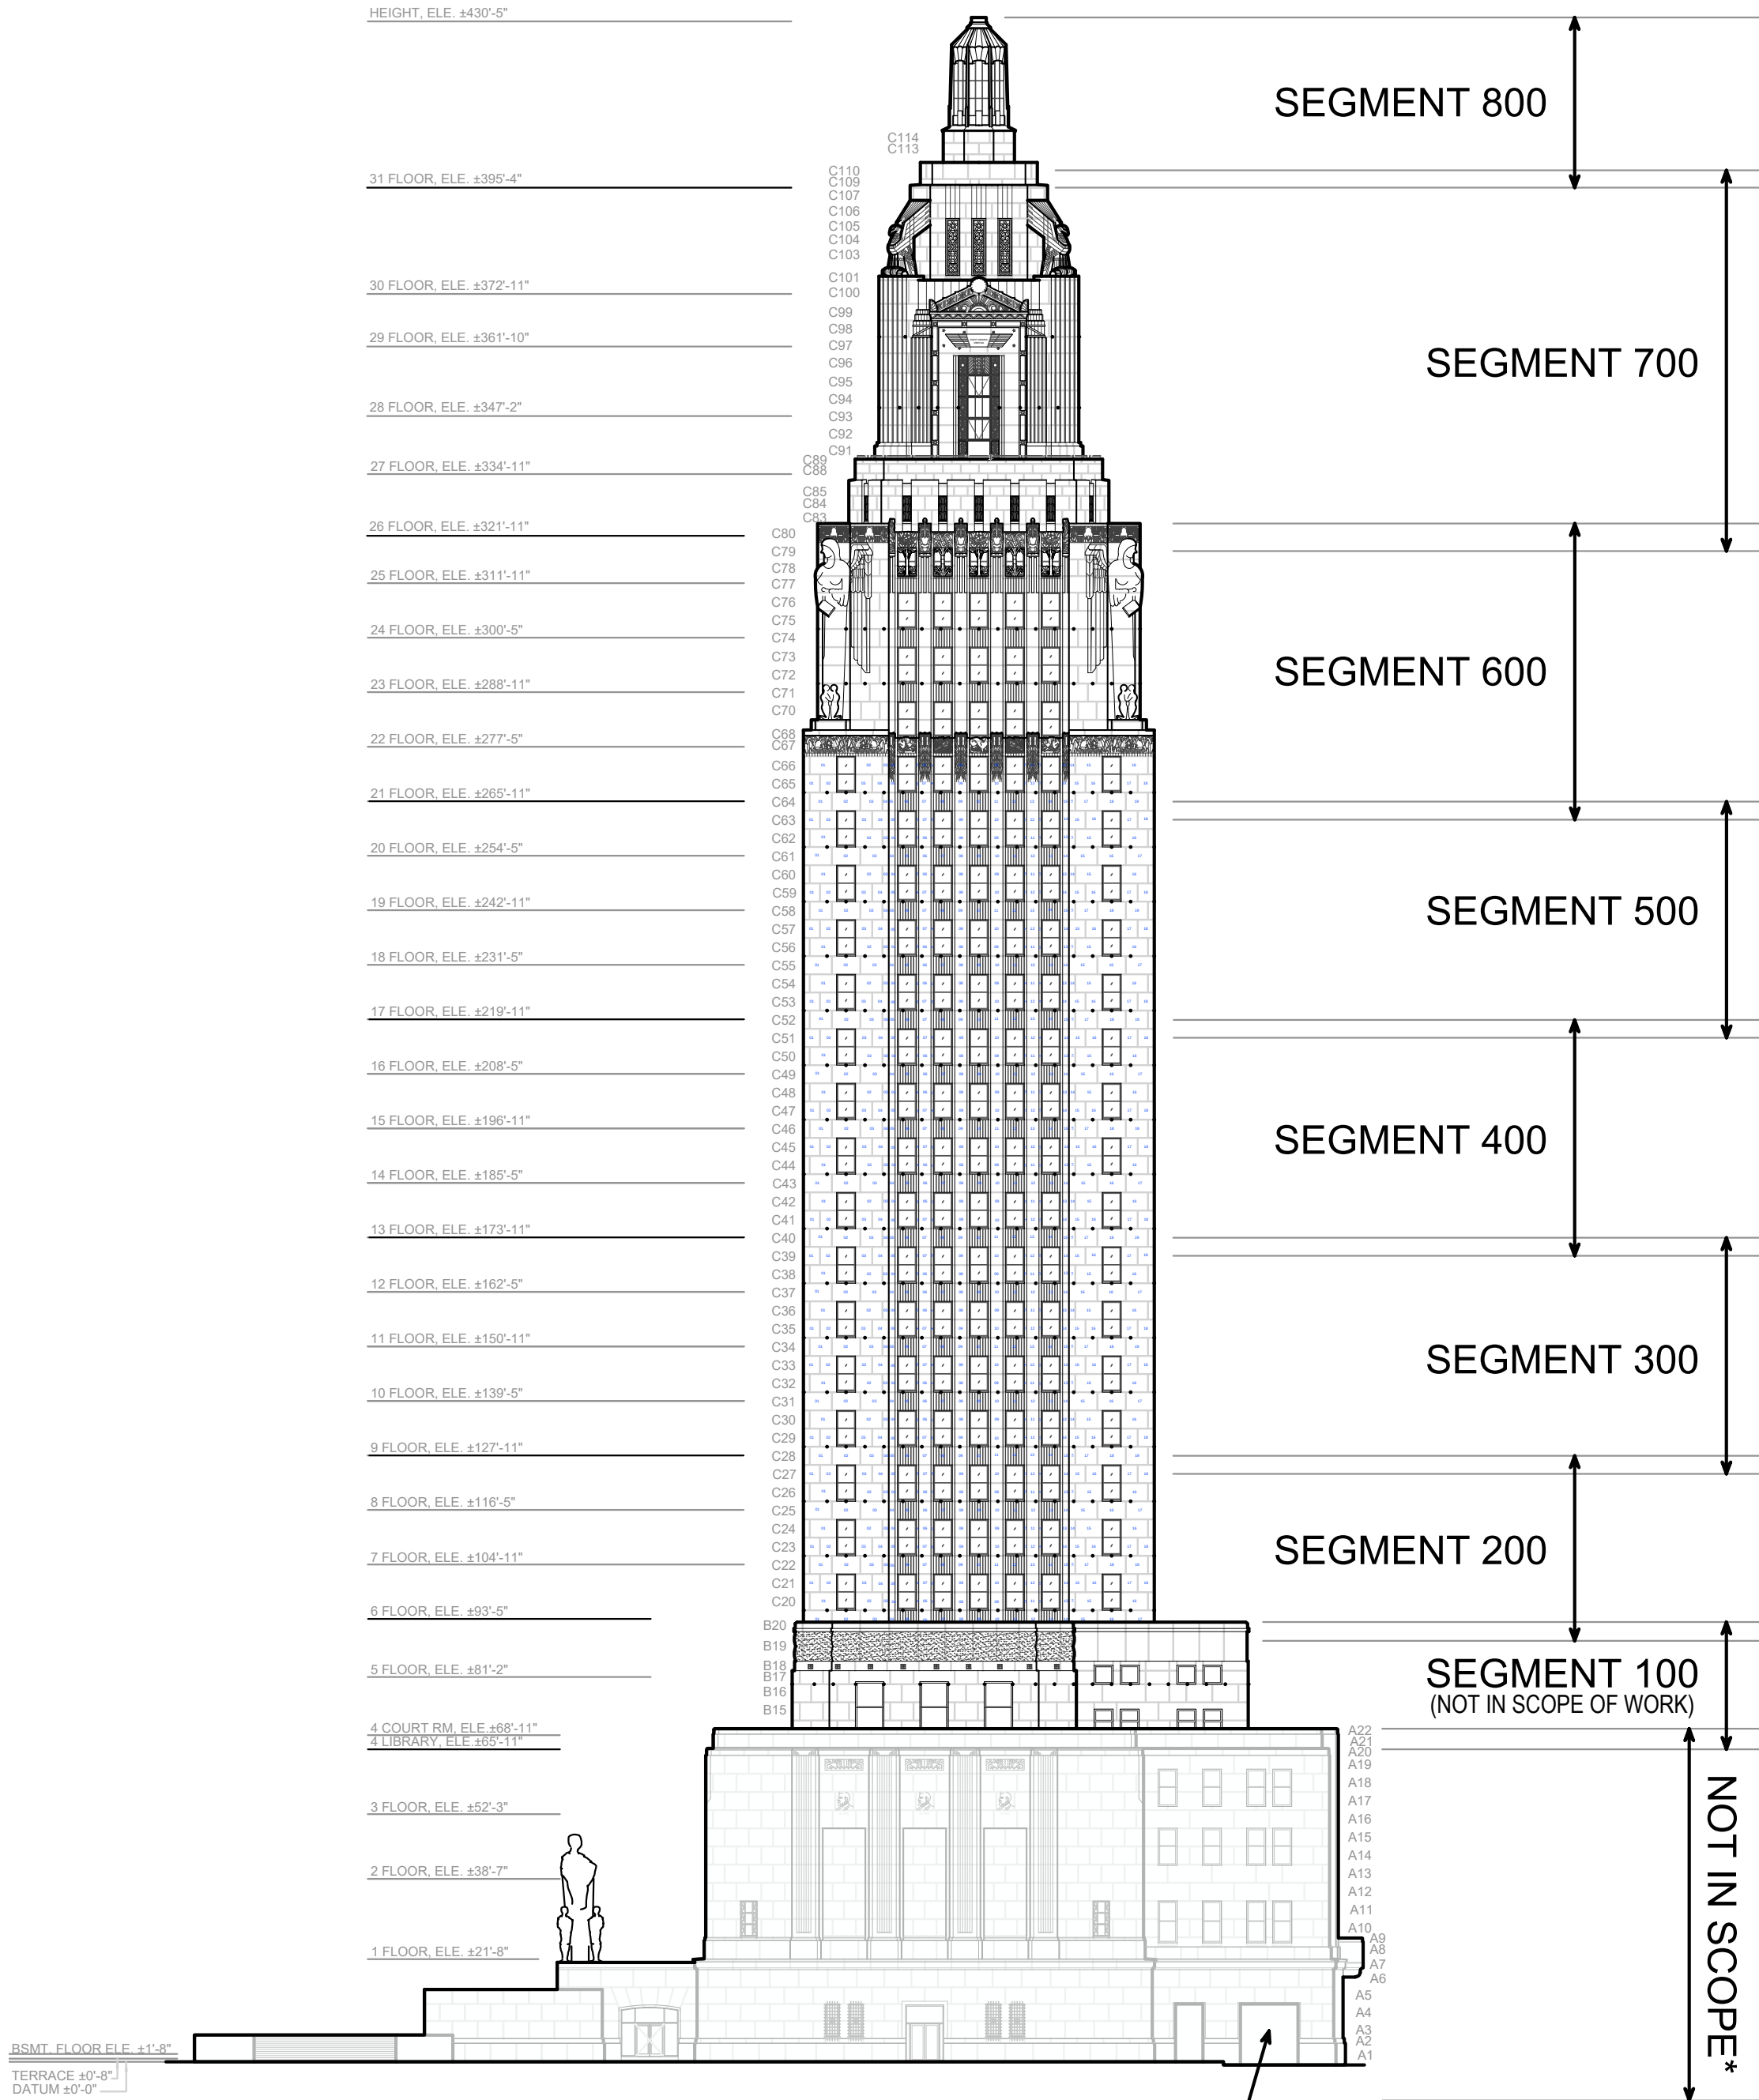


2 EAST KEY ELEVATION
SCALE: 1/4"=1'-0"

*FOUR (4) EXISTING HISTORIC OPENINGS IN THE PORTE COCHERE ARE INCLUDED IN THE ALTERNATE 1 SCOPE OF WORK. SEE SEGMENT 900.

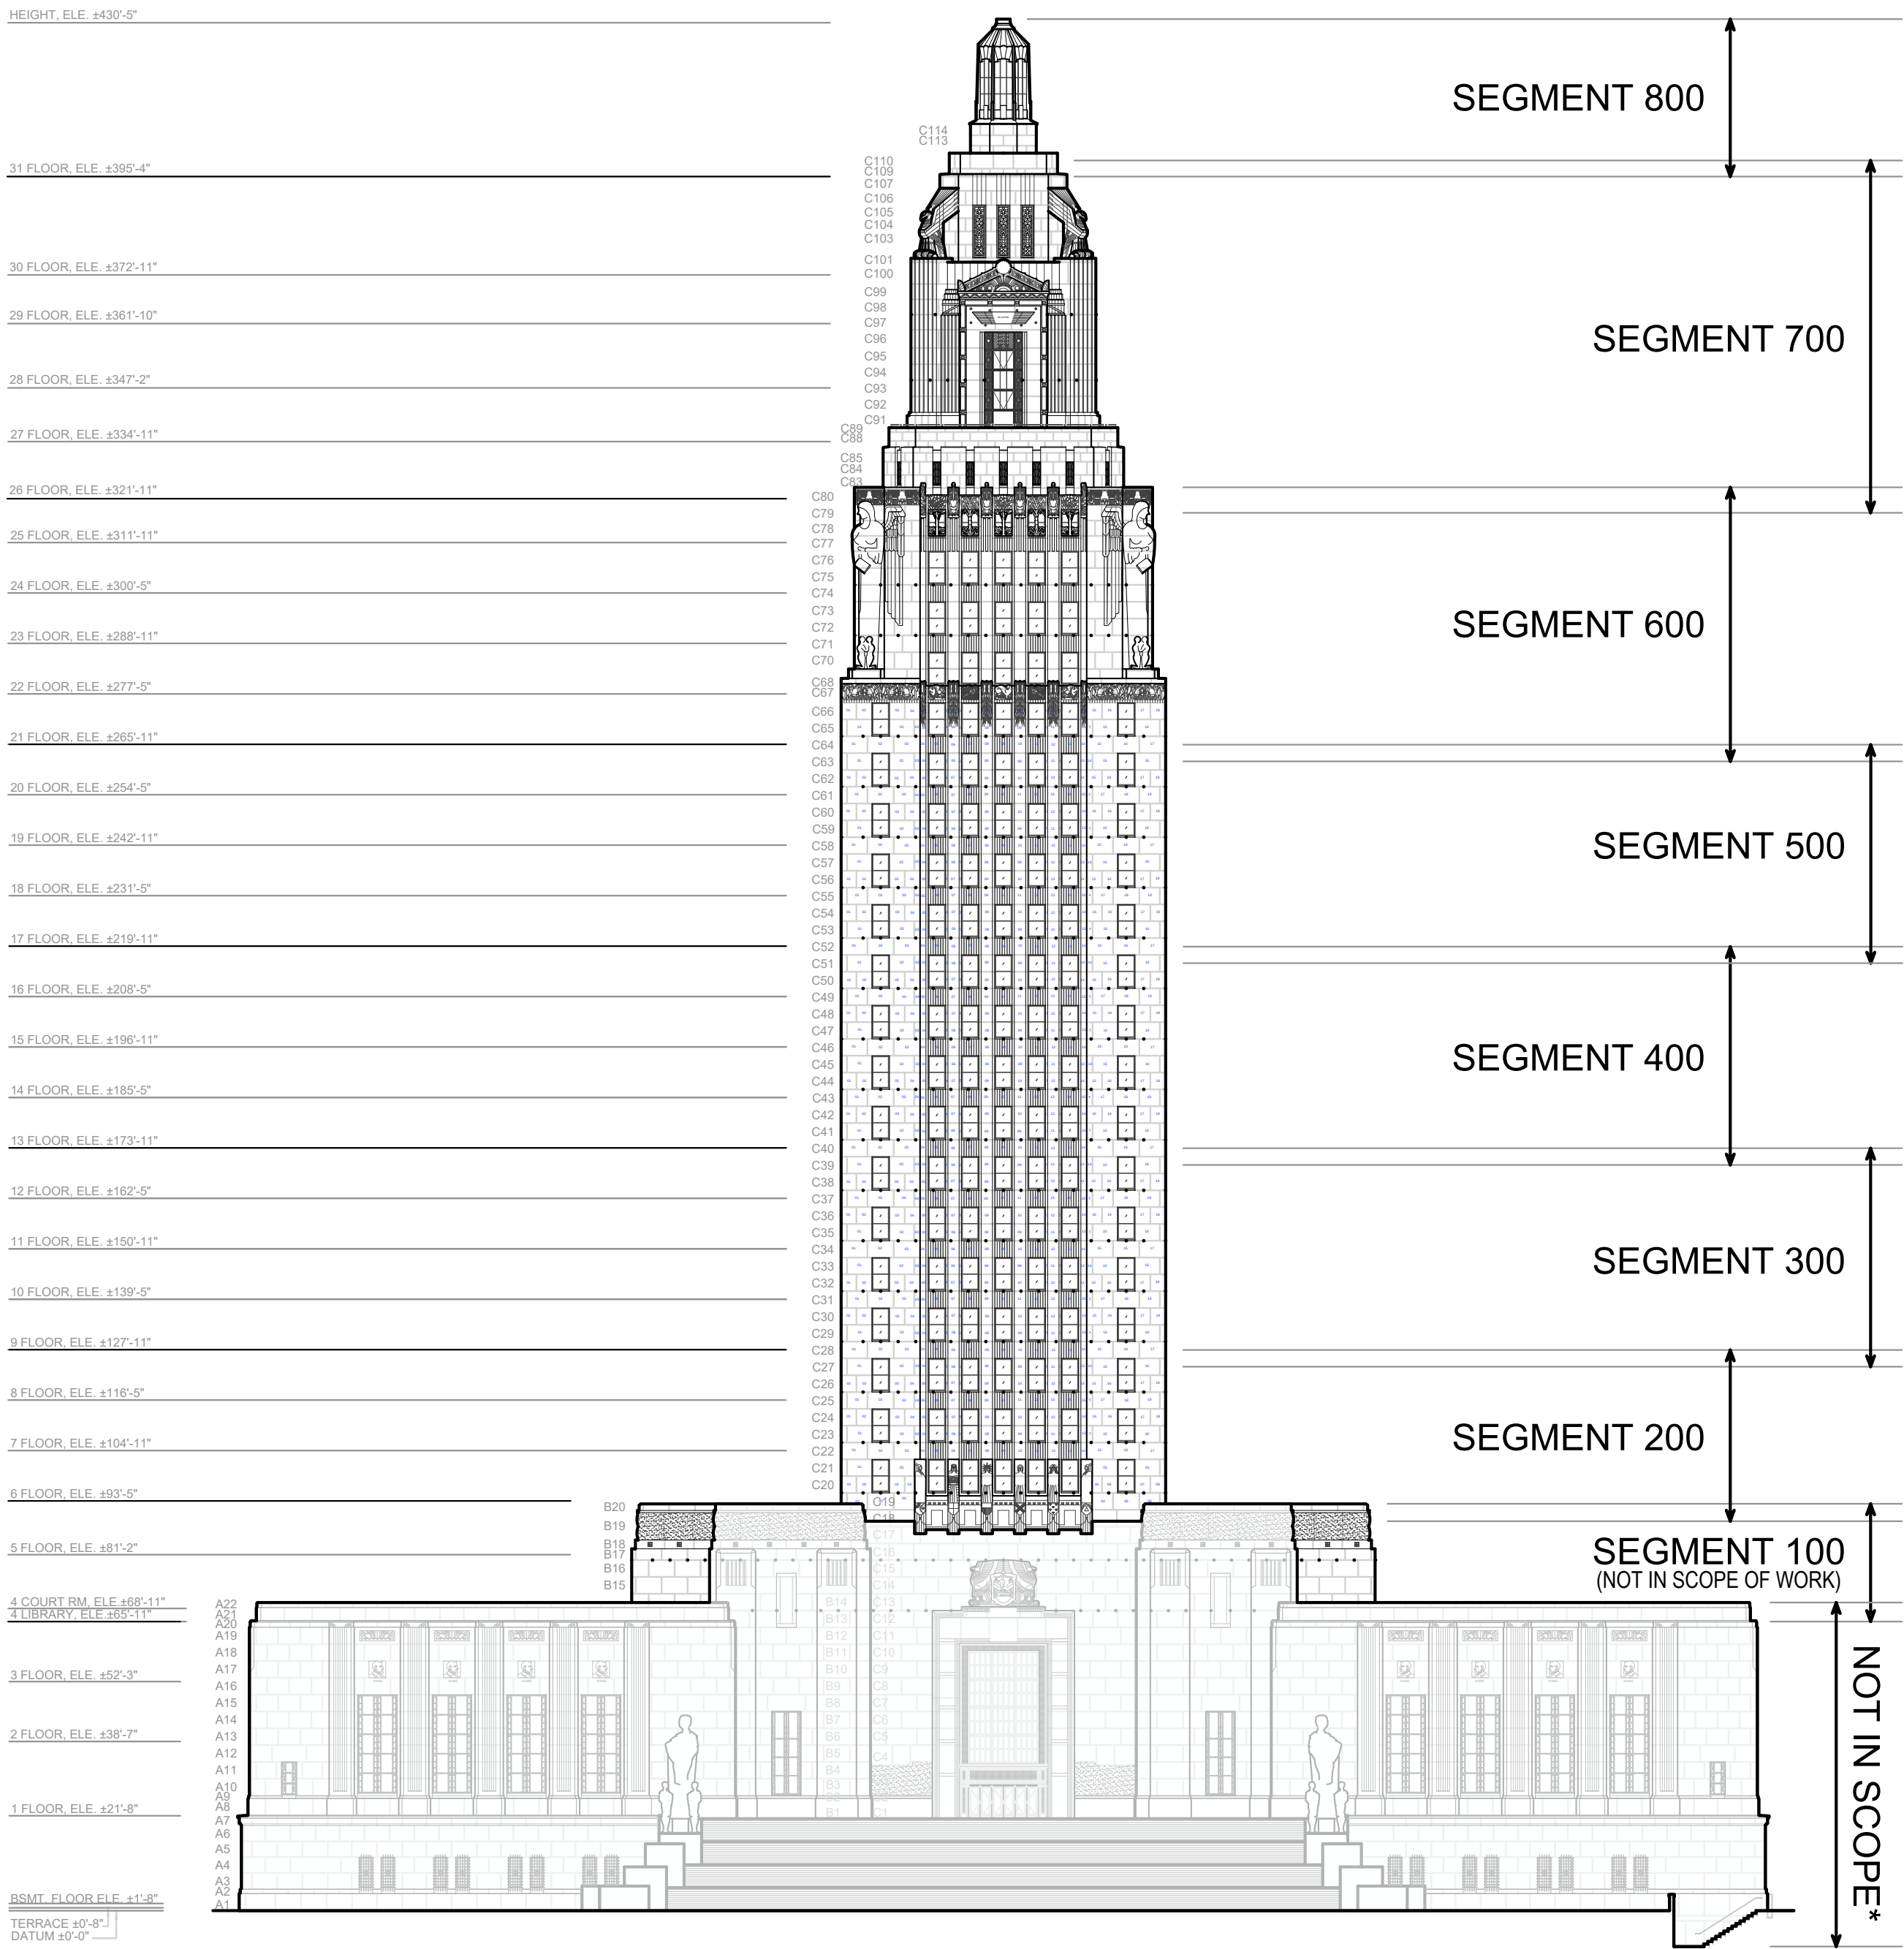


1 SOUTH KEY ELEVATION
SCALE: 1/32"=1'-0"

*FOUR (4) EXISTING HISTORIC OPENINGS IN THE PORTE COCHERE
ARE INCLUDED IN THE ALTERNATE 1 SCOPE OF WORK.
SEE SEGMENT 900.

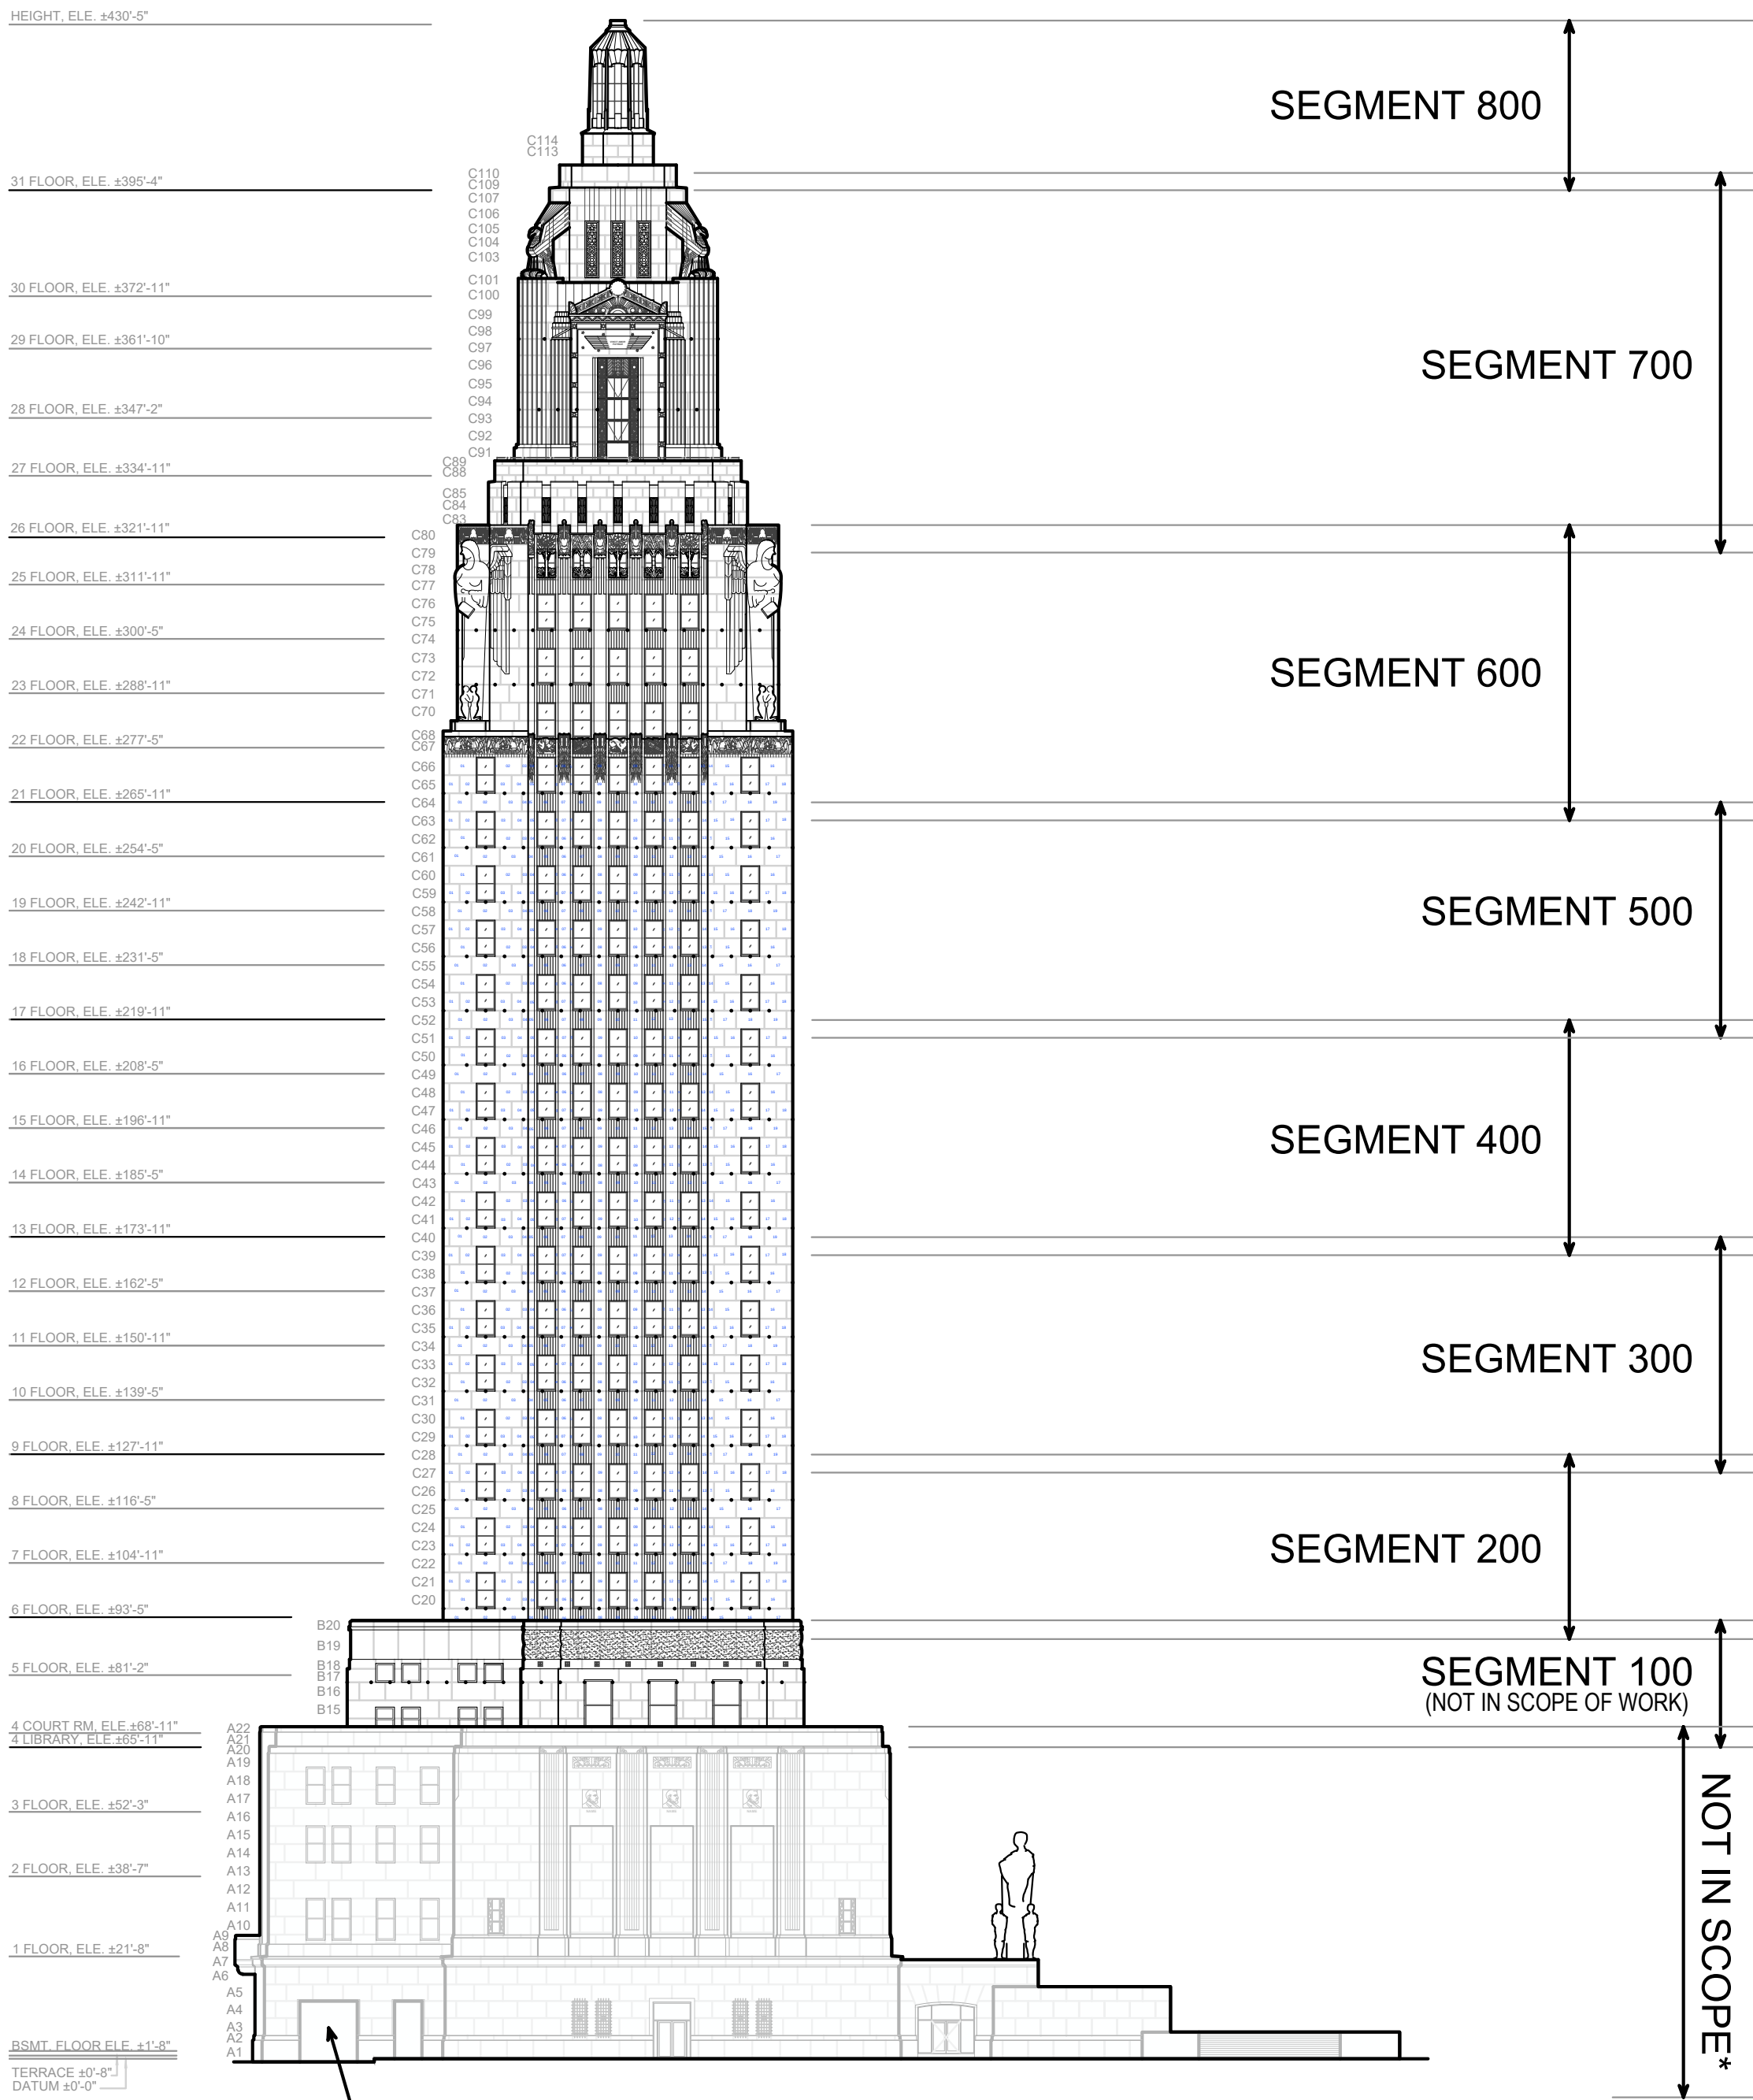

2 WEST KEY ELEVATION
SCALE: 1/4"=1'-0"

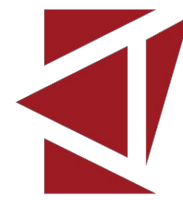

The Architectural Studio
JAMES DODDS, AIA | LANCE MALLEY, AIA
409 North 7th Street, Baton Rouge LA 70802
office: 225-215-1777
www.archstudior.com

EXTERIOR WATERPROOFING AND REROOF
SECTIONS A/B/C/F (PHASE III)
LOUISIANA STATE CAPITOL BUILDING
BATON ROUGE, LA

STATE BUILDING ID:
S02009

SITE CODE: 2-17-025

WBS No.: F.01003957

Project No. 01-107-12-01

REVISIONS

© 2025 The Architectural Studio

ARCHITECT PROJECT NO.

2659-E

CONSTRUCTION
DOCUMENTS

DECEMBER 10, 2025



[Signature]

A04

KEY ELEVATIONS 1